DOĞRAMA LİSTESİ

PROJE: ÖRNEK APARTMAN
PAFTA NO: M-10 ÖLÇEK 1/50

P-01 120/150

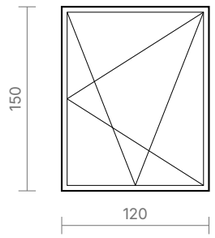

ADET: 8
PVC - RAL 9016
CAM: 4+16+4 ISICAM
AÇILIM: ÇİFT AÇILIM
PROFİL: 70 MM 5 ODACIKLI

P-02

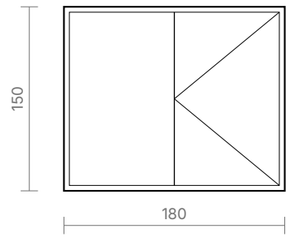

ADET: 4
PVC - RAL 9016
CAM: 4+16+4 ISICAM
AÇILIM: SABİT + AÇILIR

P-03

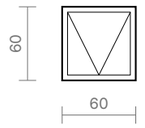

9 ADET
PVC
CAM: 4+16+4 BUZLU
AÇILIM: VASİSTAS

K-01 90/220

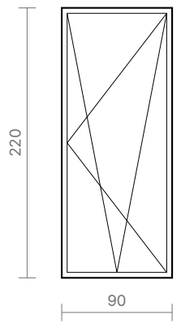

ADET: 4
BALKON KAPISI
PVC - RAL 9016
CAM: 4+16+4 TEMPERLİ

S-01

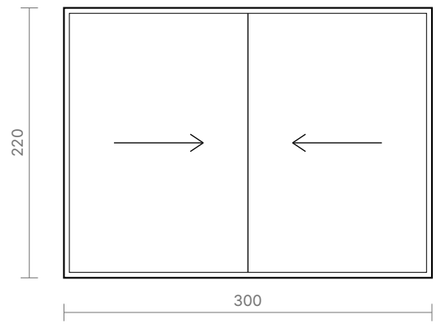

MİKTAR: 4 AD.
SÜRME KAPI
ALÜMİNYUM - RAL 7016 ANTRASİT
SİSTEM: ISI YALITIMLI SÜRME SERİ
CAM: 6+16+6 TEMPERLİ

CP-01

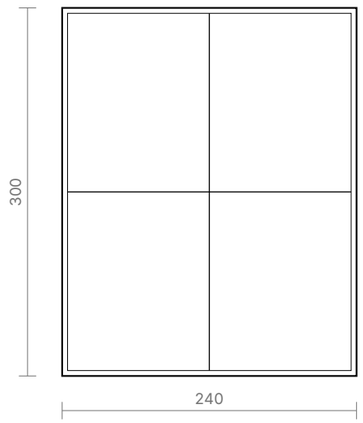

ADET: 2
GİYDİRME CEPHE - ZEMİN KAT
ALÜMİNYUM - RAL 7016
CAM: 6+16+6 LOW-E

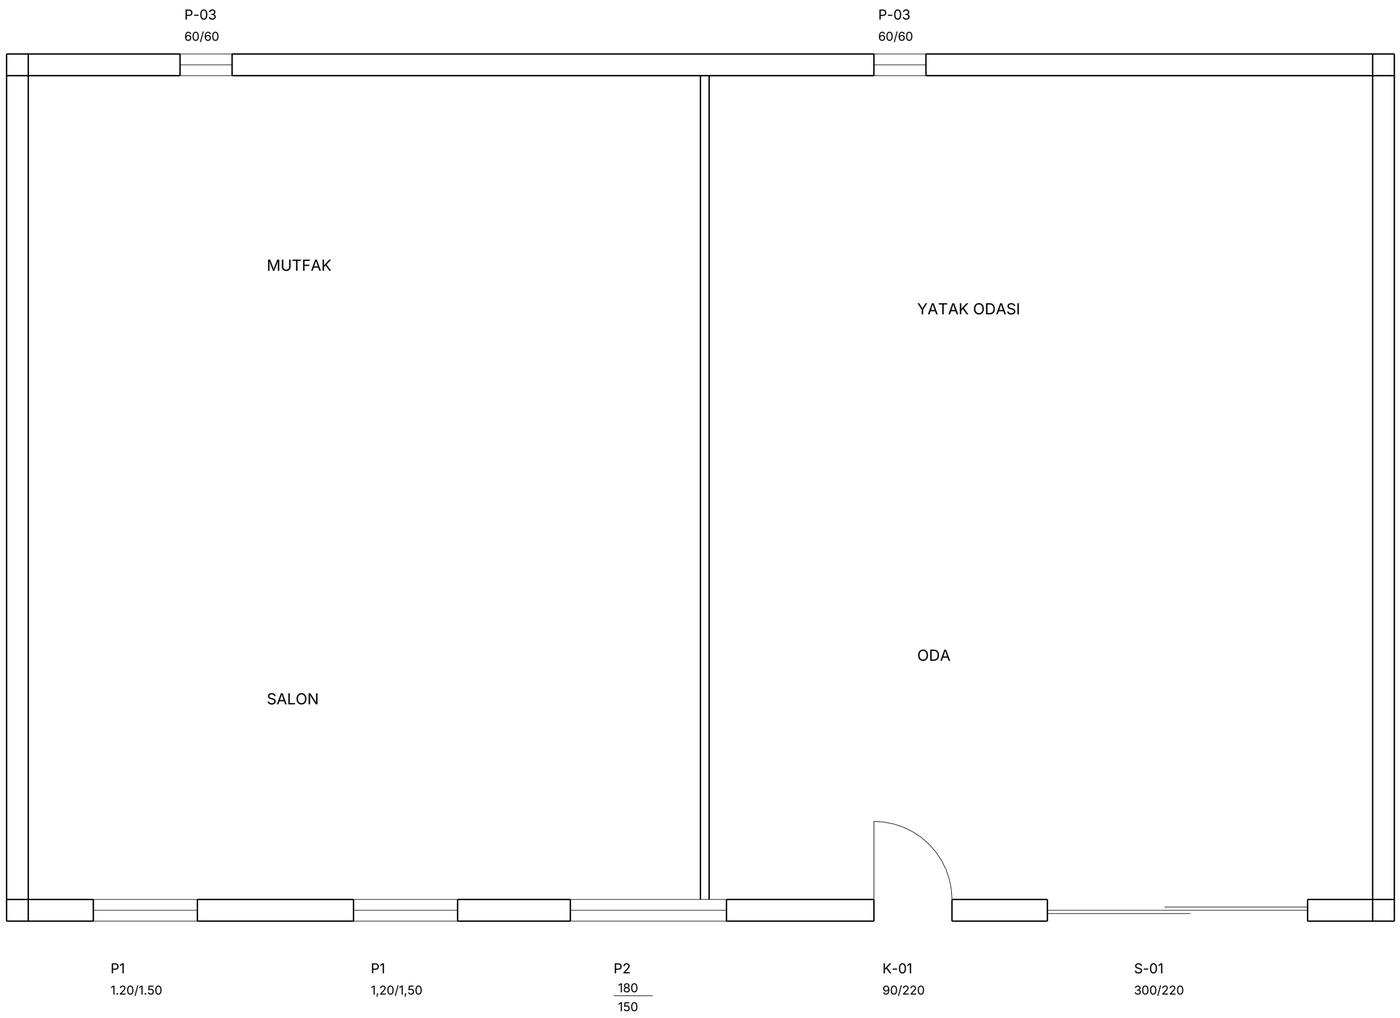

NOT: AKSİ BELİRTİLMEDİKÇE TÜM DOĞRAMALAR PVC, RAL 9016 BEYAZDIR.

PROJE: ÖRNEK APARTMAN

PAFTA: NORMAL KAT PLANI (1.-4. KATLAR)

ÖLÇEK 1/50

PAFTA NO: M-02